
SUPPLY SCOPE: Nudura ICF forms, accessories, pre-cut service, alignment hire and haulage as the quotation only. Block and beam floors, partitions, the vaulted roof, oak trusses, steels and the chimney support steel are shown in good faith for coordination only and must be checked by the relevant professional (engineer / specialists).

QUOTATION - NOT FOR CONSTRUCTION

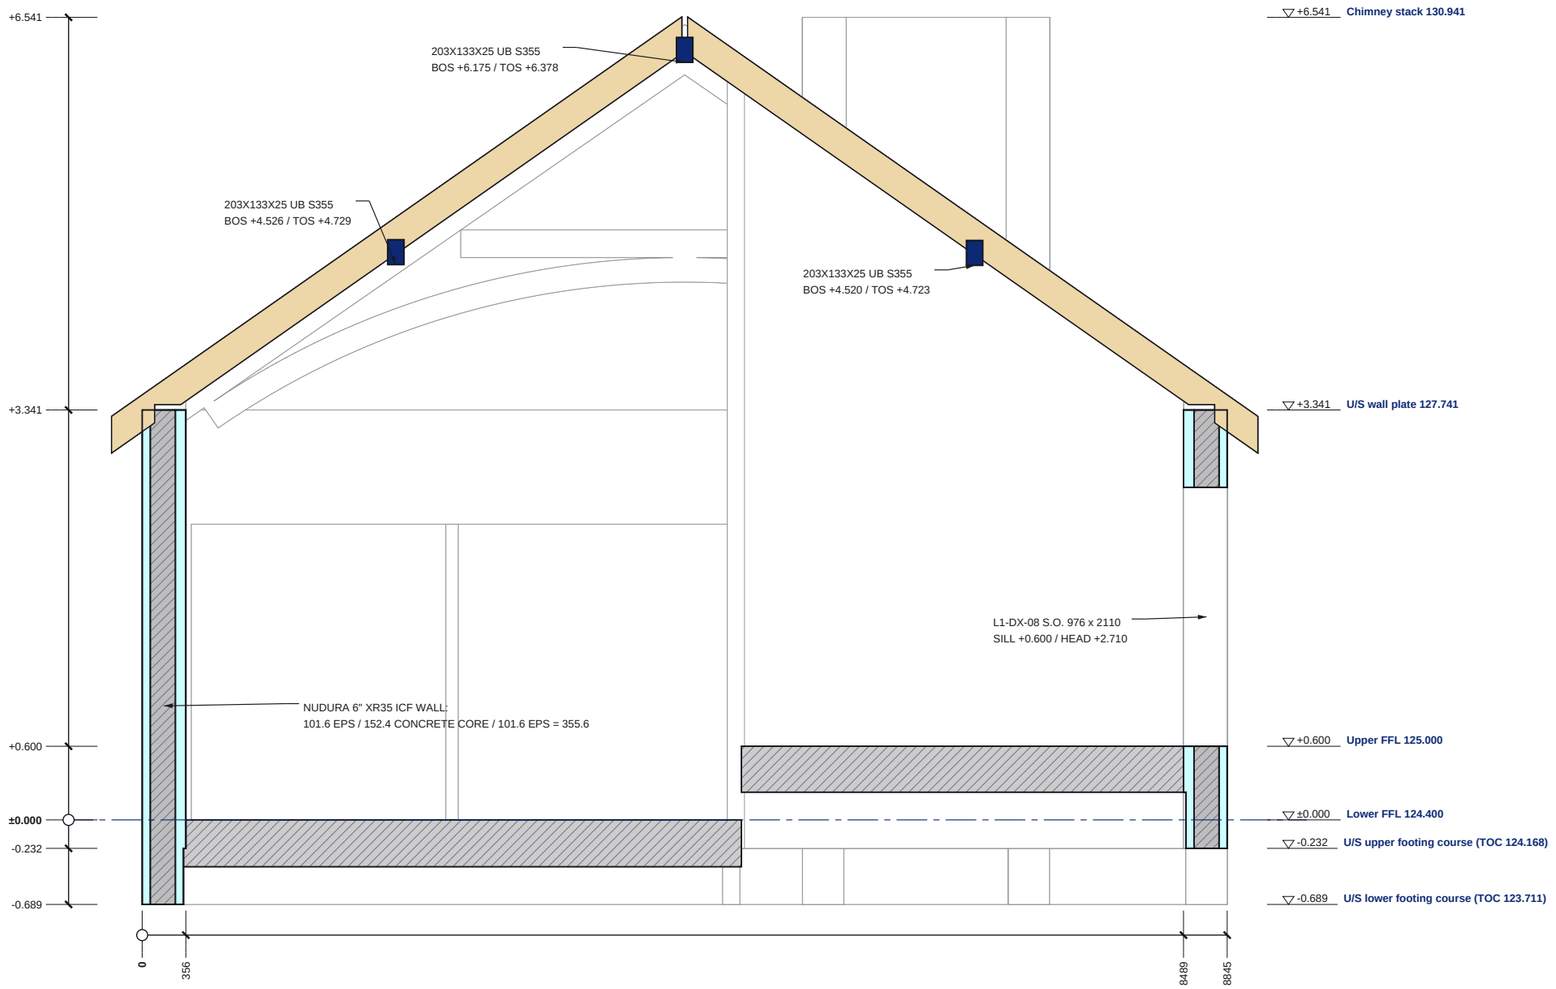

SECTION A-A

Scale 1:50 @ A3 | Looking west; levels above GF FFL

ICF EPS (cut)
ICF concrete core / RC (cut)
Steel (cut)
Blinding / hardcore
Masonry wall (cut)
Beyond the cut (line work)

0 1 2m

SECTION A-A SCHEDULES


LEVELS ON THIS SECTION

Level	FFL
U/S lower footing course (TOC 123.711)	-0.689
U/S upper footing course (TOC 124.168)	-0.232
Lower FFL 124.400	±0.000
Upper FFL 125.000	+0.600
U/S wall plate 127.741	+3.341
Chimney stack 130.941	+6.541

STEEL CUT BY THIS SECTION

Mark	Section (engineer)	BOS	TOS
-	203x133x25 UB S355	+6.175	+6.378
-	203x133x25 UB S355	+4.520	+4.723
-	203x133x25 UB S355	+4.526	+4.729

SECTION KEY

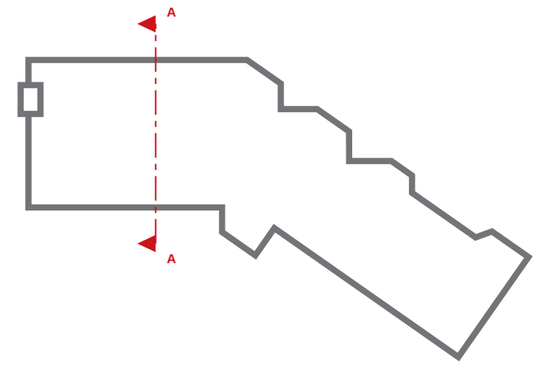

NOTES

1. Section A-A is a BuildEase ICF section (not an architect's section line). Cut elements hatched / filled; the model beyond the cut in line work.
2. Levels above GF FFL.
3. ICF: Nudura 6" XR35, 101.6 EPS + 152.4 core + 101.6 EPS = 355.6; 8" Std, 66.7 EPS + 203.2 core + 66.7 EPS = 336.6, 203.2 core + 66.7 EPS = 336.6. No structural design yet. ICF per the quotation model: one 8in Standard footing course in each floor zone (lower 124.40 kitchen / dining / snug, upper 125.00 elsewhere), block and beam bearing on it with a 150 mm inside-face cut, 6in XR35 above to the wall plate (127.741), gables raked to the 35 degree roof, the chimney stack to 130.941 and the walls set back from the eaves raised to the vaulted roof. Stack support steel, ridges, purlins, oak trusses and posts for the engineer.
4. Steel marks, BOS / TOS: rev -. See ES26-063-GA-01 / EL-01 / EL-02 in the approval drawings pack.

REVISIONS

REV	DATE	DESCRIPTION
-	02.11.26	First issue - with the Nudura proposal Rev A

Nudura™ BuildEase

CLIENT	PROJECT
Ethos Property Development	Langley Lane Farm, Langley Lane, Middleton M24 5LJ

DRAWING TITLE
SECTION A-A

ICF section with levels and build-ups

SCALE	SIZE	DATE
1:50	A3	02.11.26
DRAWN	CHECKED	APPROVED
TS		

STATUS	DRAWING No.	REV
QUOTATION	ES26-063-SE-01	-

Do not scale. All dimensions in millimetres, levels in metres from GF FFL. Check all dimensions on site.